
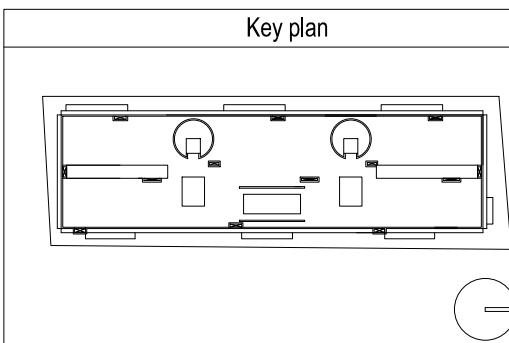


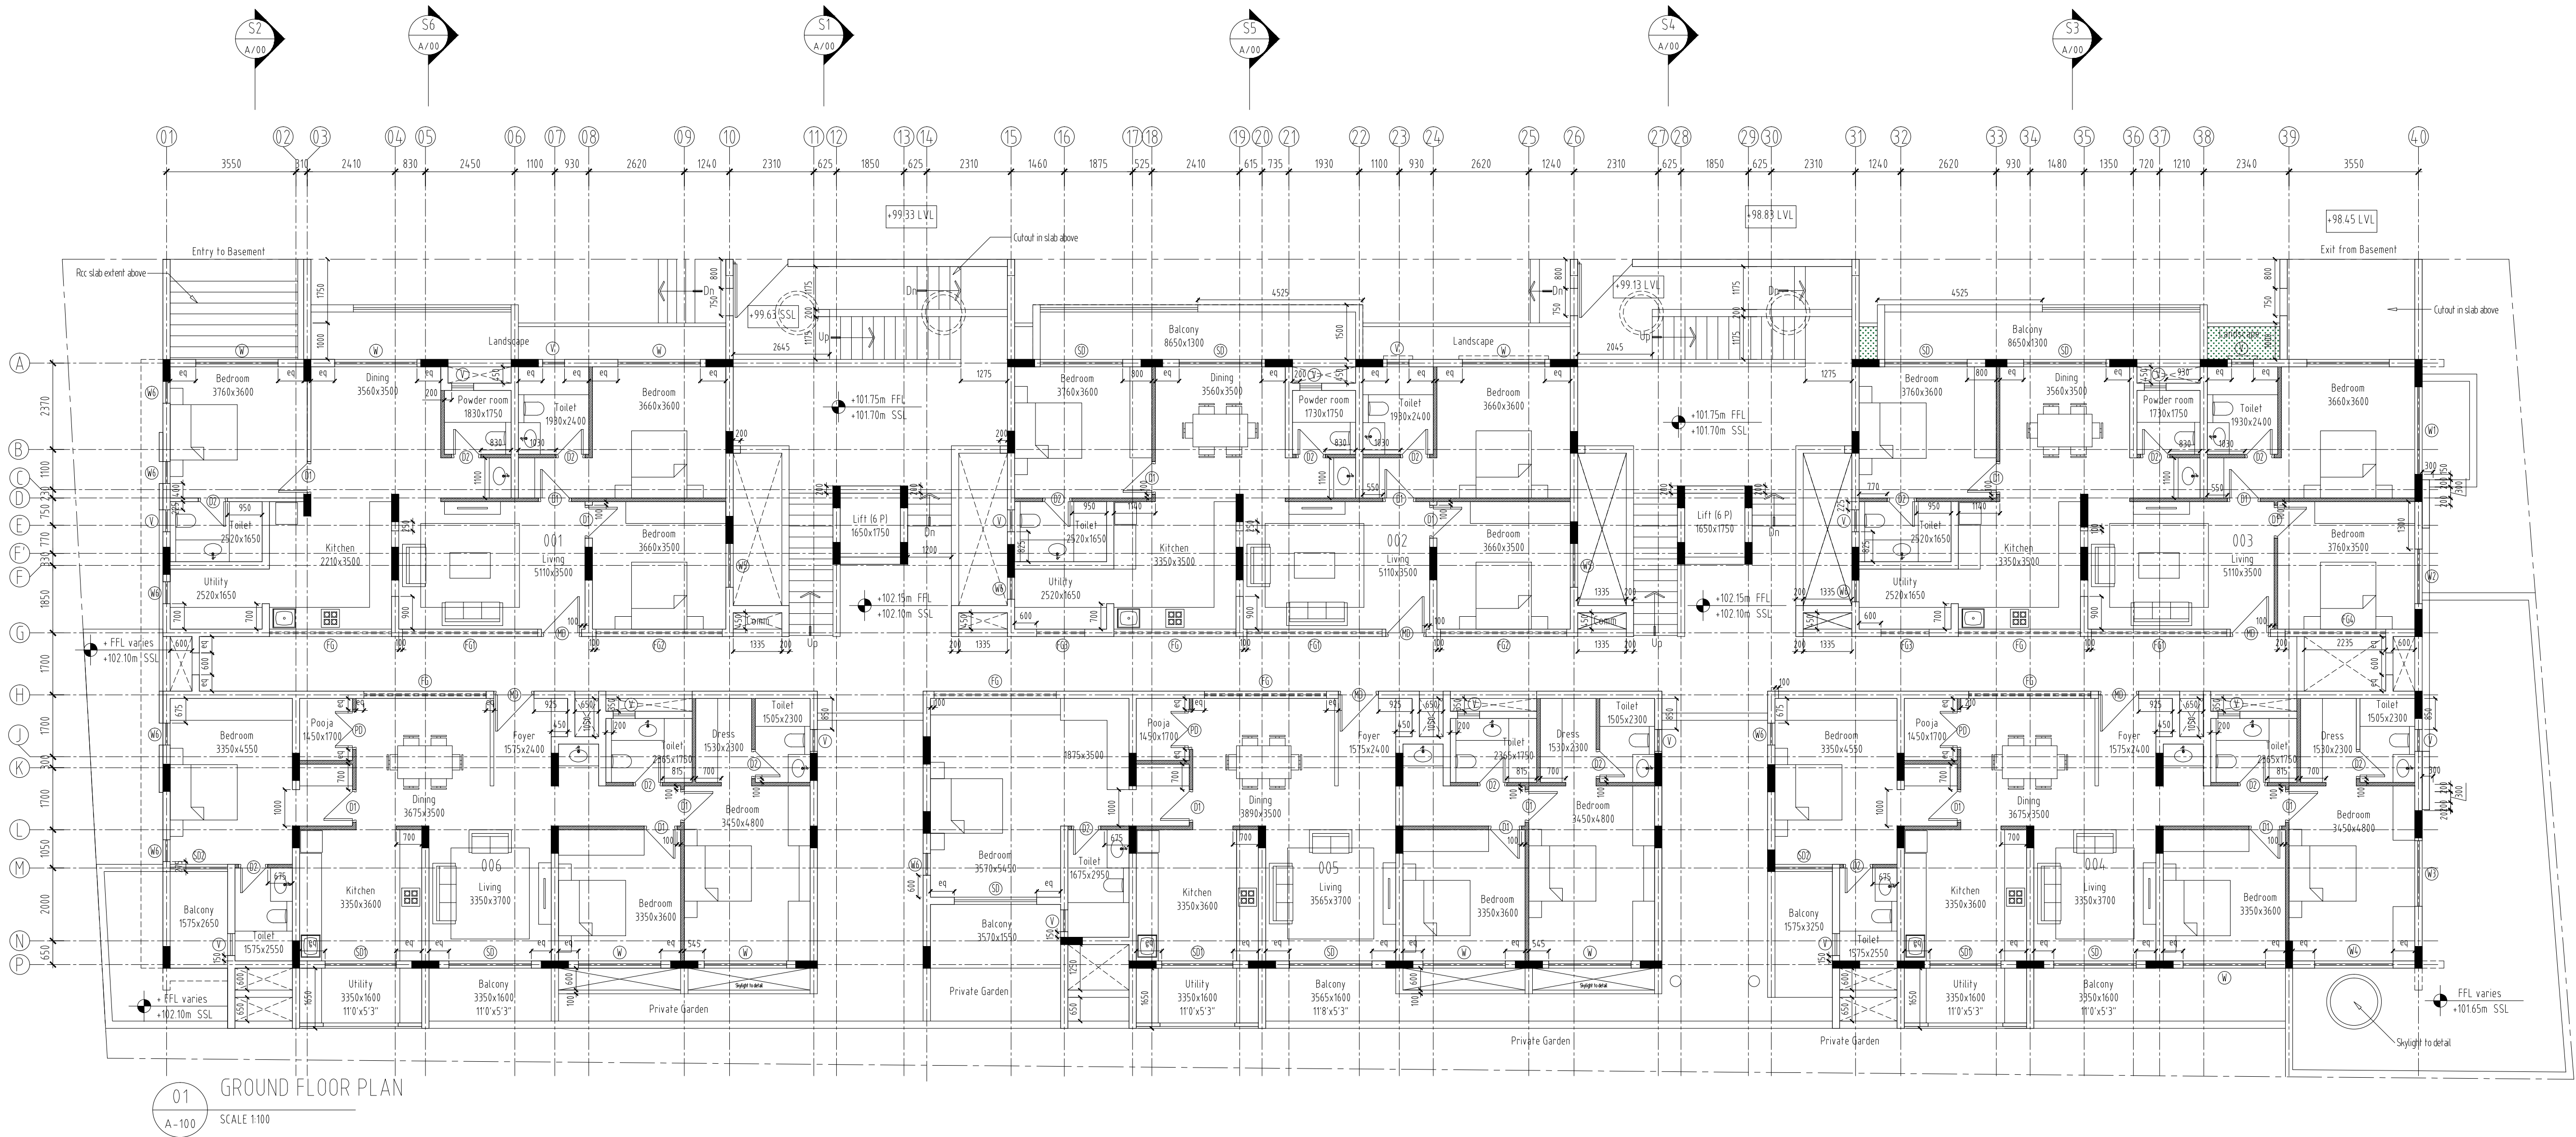

General Notes

1. All dimensions are in millimeters and levels in meters unless noted otherwise.
2. Any discrepancies in the drawing shall be brought to the notice of the architect before execution.
3. All dimensions to be verified on site and approved by the Project manager.
4. Drawing should be read in conjunction with other relevant Architectural, Structural and Electrical drawings and all relevant sections.

Schedule of Openings:		
Doors	Description	
	Cill height	Lintel height
MD - 1100X2150	-	2150
DD - 1500X2150	-	2150
PD - 1100X2150	-	2150
D1 - 900X2150	-	2150
D1a - 1100X2150	-	2150
D2 - 1800X2150	-	2150
Sliding Door		
SD - 2260X2150	-	2150
SD1 - 1950X2150	-	2150
SD2 - 1575X2150	-	2150
SD3 - 2400X2150	-	2150
SD4 - 1800X2150	-	2150

Windows		
W - 2260X1500	650	2150
W1 - 2400X1500	650	2150
W2 - 1500X1500	650	2150
W3 - 1800X1500	650	2150
W4 - 2150X1500	650	2150
W5 - 1200X1500	650	2150
W6 - 600X1500	650	2150

Fixed Glass		
FG - 3350X400		Beam Bottom
FG1 - 3710X400		Beam Bottom
FG2 - 3460X400		Beam Bottom
FG3 - 1320X400		Beam Bottom
FG4 - 2760X400		Beam Bottom
FG5 - 3150X400		Beam Bottom

Ventilators		
V1 - 600X600	1550	2150

Notes:

01. Lintel height mentioned is from SSL.
02. Toilets are 100mm sunk.
03. Utilities are 200mm sunk.
04. Balconies are 200mm sunk.

Revisions:		

Purpose of issue:

Good for Construction

Project

TB TOWERS
Proposed Apartments
Davangere

Drawing Number

AR-003

Date

25 August 2025

Drawing Title:

Ground Floor plan

Scale	1:100
Drawn	BB
Checked	AC
Approved	AC

Architects:

Design Front Architects,
Architecture, Planning, Interiors Landscape
1/2, 2nd Main Road, Palace Cross Road,
Chandavarkar Layout, Bangalore - 560 020
Tel: 91-80-23566878