

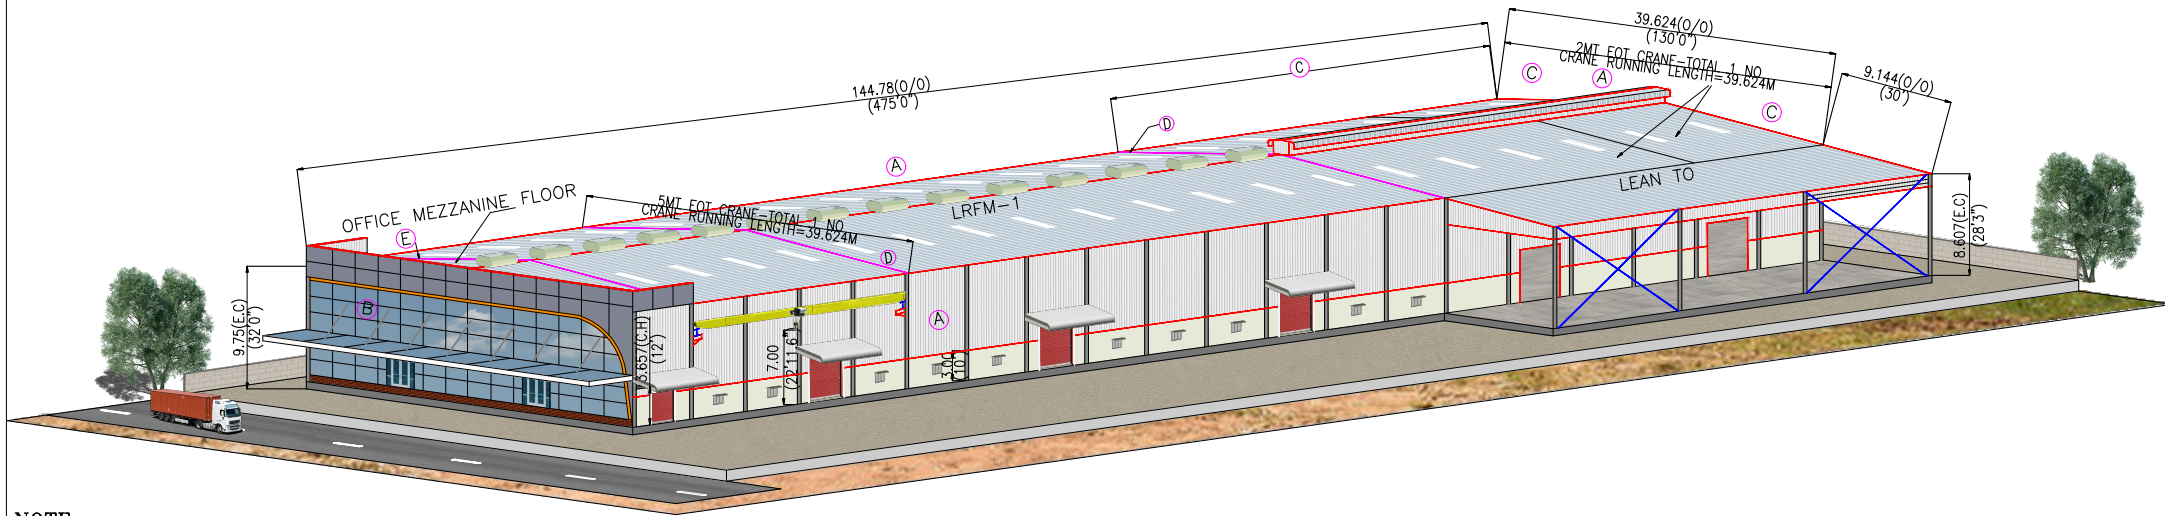


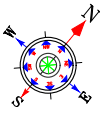

NOTE :-

1. WALL LOUVERS, WALL LIGHTS & TURBO FAN SHOWN ABOVE ARE FOR PRESENTATION PURPOSE ONLY. THESE COMPONENTS STANDS CONSIDERED ONLY IF MENTIONED IN TECHNO COMMERCIAL OFFER.
2. ALL DIMENSIONS ARE IN METERS U.N.O
3. SLOPE:-1:08(DOUBLE SLOPE-LRFM-1 WITH LEAN TO).
4. (A) 3.00M HEIGHT BRICK WALL AND REST METAL CLADDING.
5. (B) FULL HEIGHT GLAZING.
6. CLIENT SCOPE:- GLAZING CANOPY.
7. CANOPY PROJECTION(3.30M).
8. ROOF RIDGE VENTILATOR 3.00M LENGTH TOTAL=14 NUMBERS.
9. ROOF MONITOR.
10. OFFICE MEZZANINE FLOOR SIZE=39.62MXONE BAY, CH=12'0").
11. LEAN TO FULL HEIGHT OPEN AND REST GABLE END SHEET.
12. FASCIA
13. (C) INDUSTRIES LOUVERS:- DOUBLE FINNED.
14. (D) PARTITION WALL:-3.00M HEIGHT BRICK WALL AND REST METAL CLADDING.
15. (E) PARTITION WALL:-FULL HEIGHT BRICK WALL

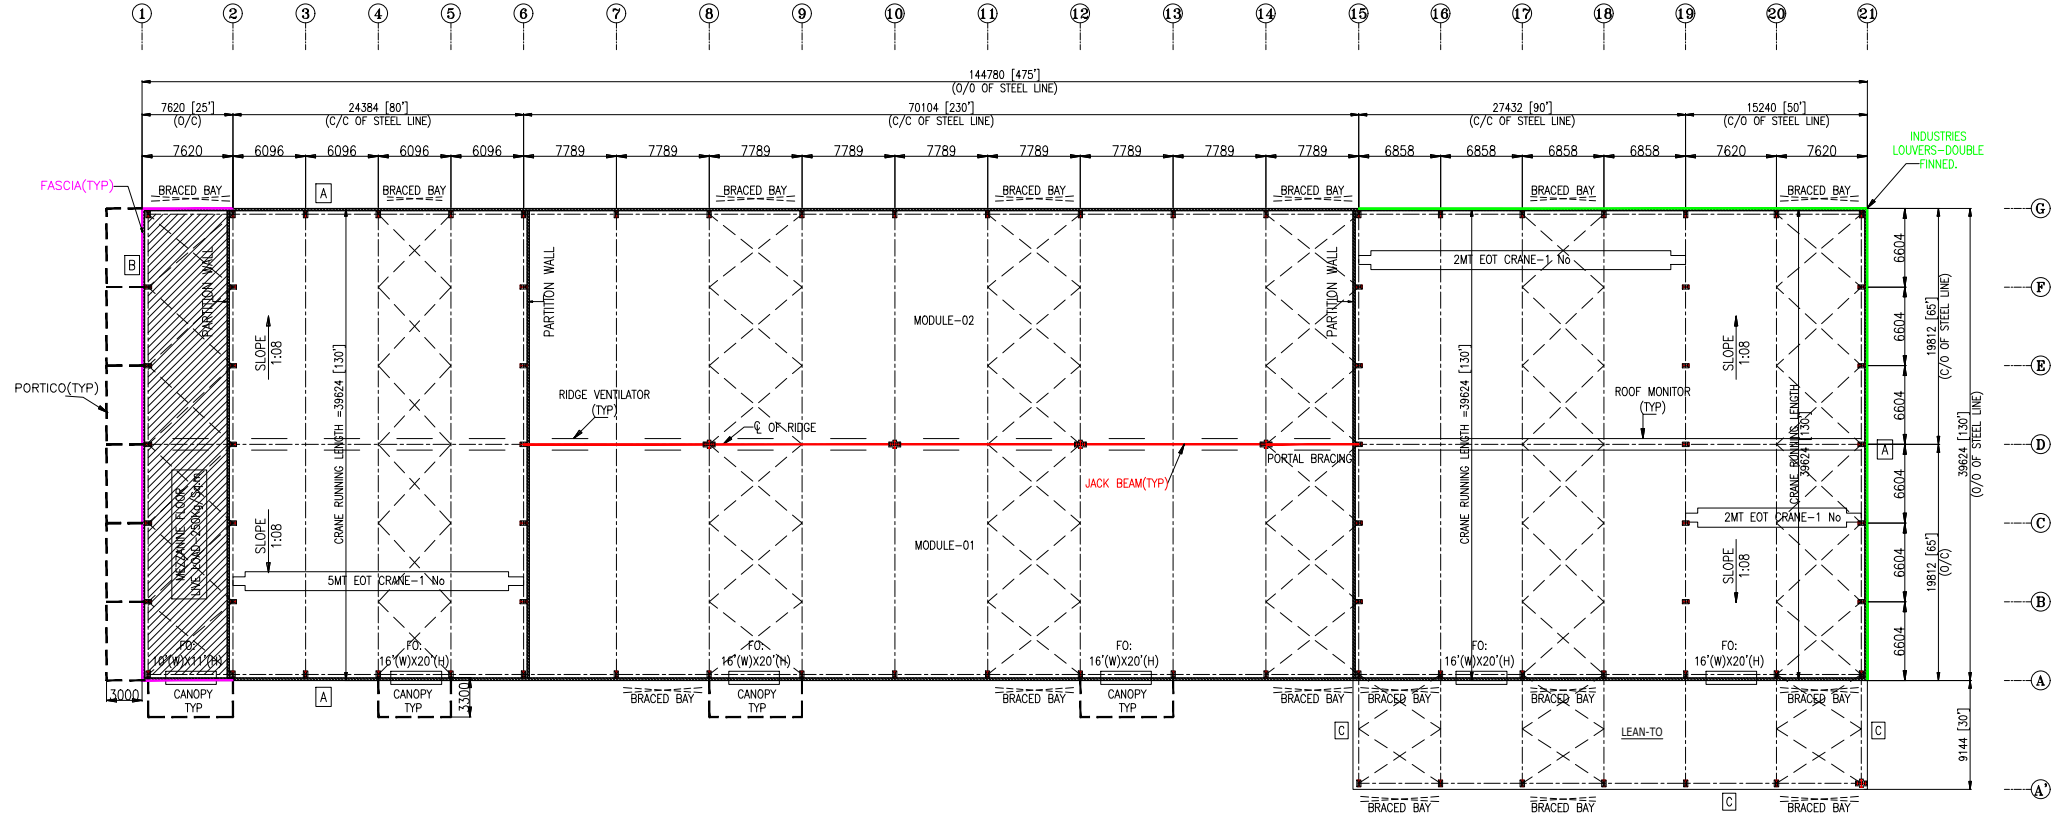


GA-PLAN


NOTE :-

1. ALL DIMENSIONS ARE IN MM U.N.O
2. BASE PLATE SIZE NOT IN TRUE SCALE
3. [A] 10' BRICK WALL REST METAL CLADDING.
4. [B] 10' BRICK WALL REST GLAZING.
5. [C] FULL HEIGHT OPEN GABLE END SHEETING.

HalleysBlue™ Pre Engineered Buildings
#57, Mundargi Industrial Area, 2nd Stage, B'lore Road, Bellary, Karnataka, India.
Ph: 9972576888, Email: sachin.n@halleysblue.in, Web: www.halleysblue.com

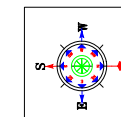

TITLE	PROJECT:				
	Fasteners & Allied Products Pvt Ltd, Hubli,				
GA-PLAN	DATE	DRAWN	APPROVED	DRG NO.	REV NO.
	14/01/26	AV	SA	PR-03	02

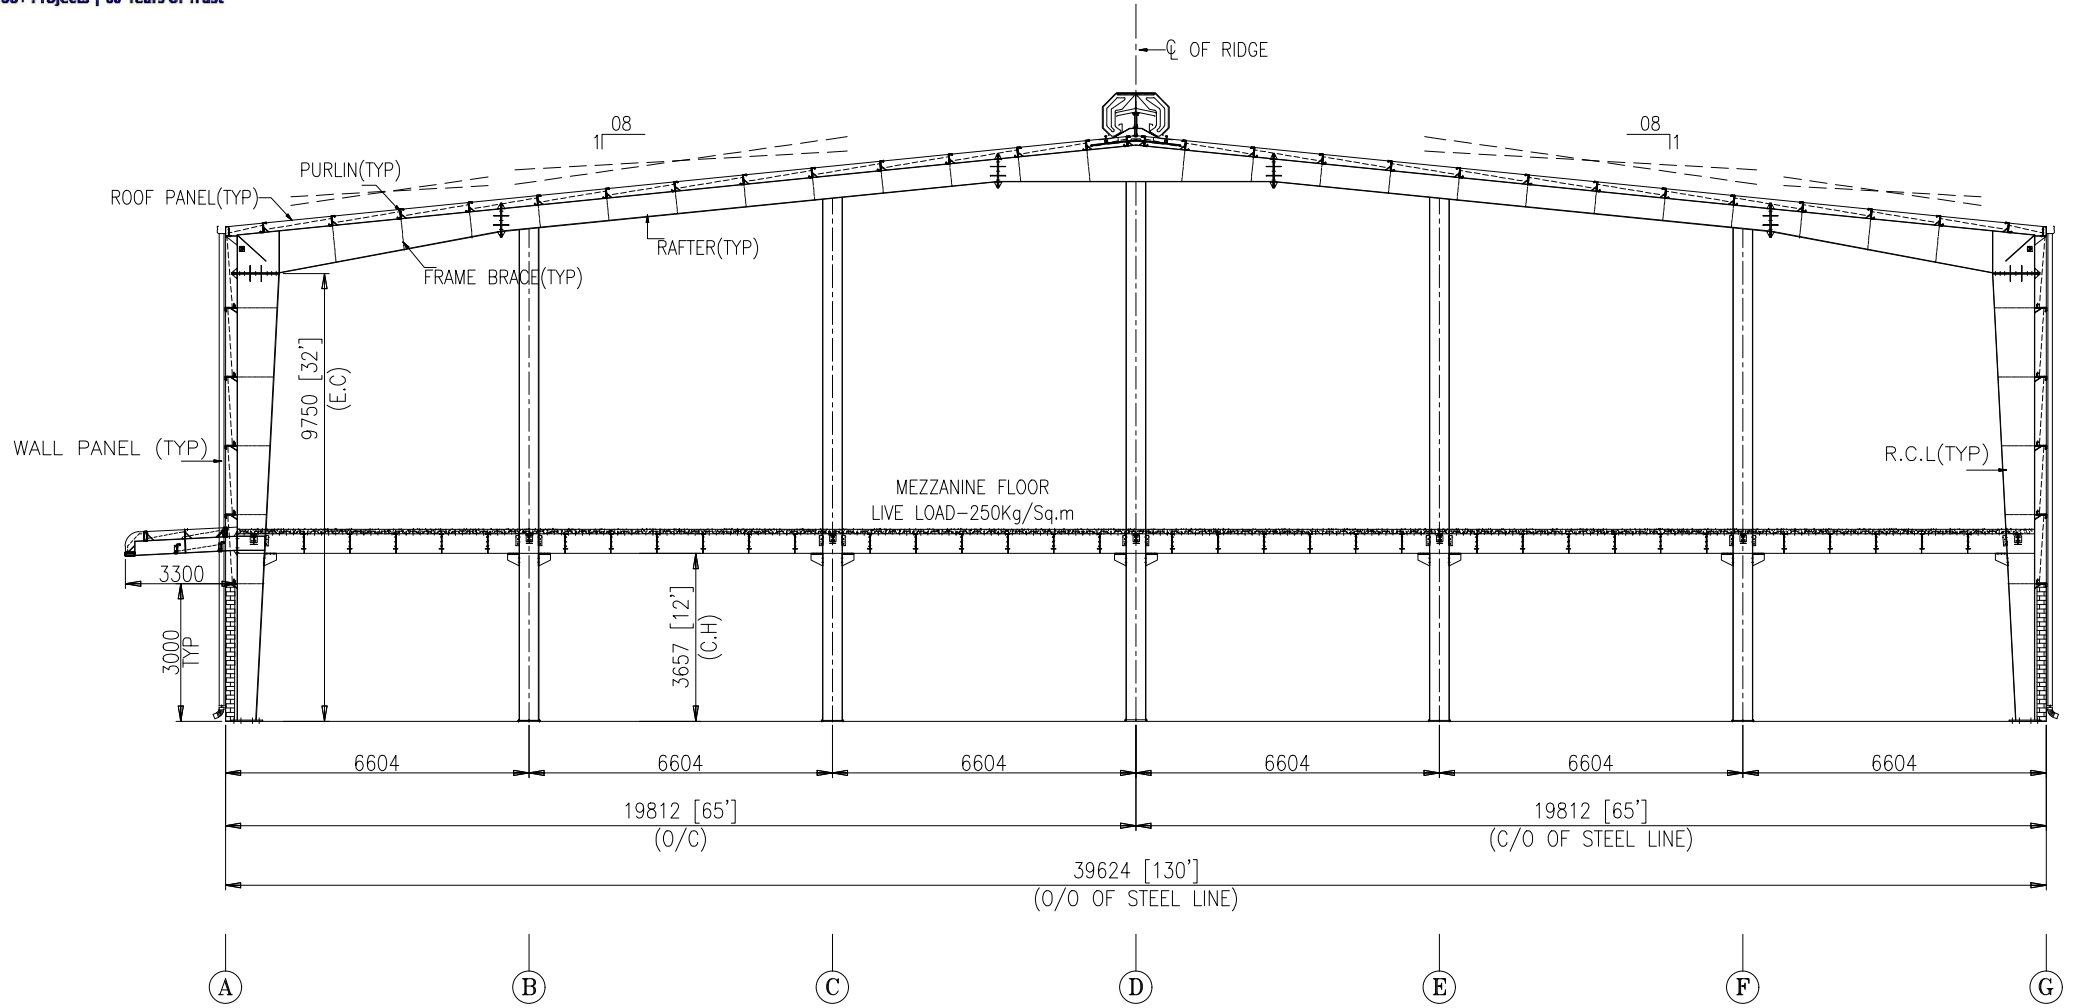


CROSS SECTION AT FRAME LINE-02

NOTE :-

1. ALL DIMENSIONS ARE IN MM U.N.O
2. BASE PLATE SIZE NOT IN TRUE SCALE

TITLE PEB	PROJECT: Fasteners & Allied Products Pvt Ltd, Hubli,				
	CROSS SECTION	DATE 14/01/26	DRAWN AV	APPROVED SA	DRG NO. PR-03
					REV NO. 02

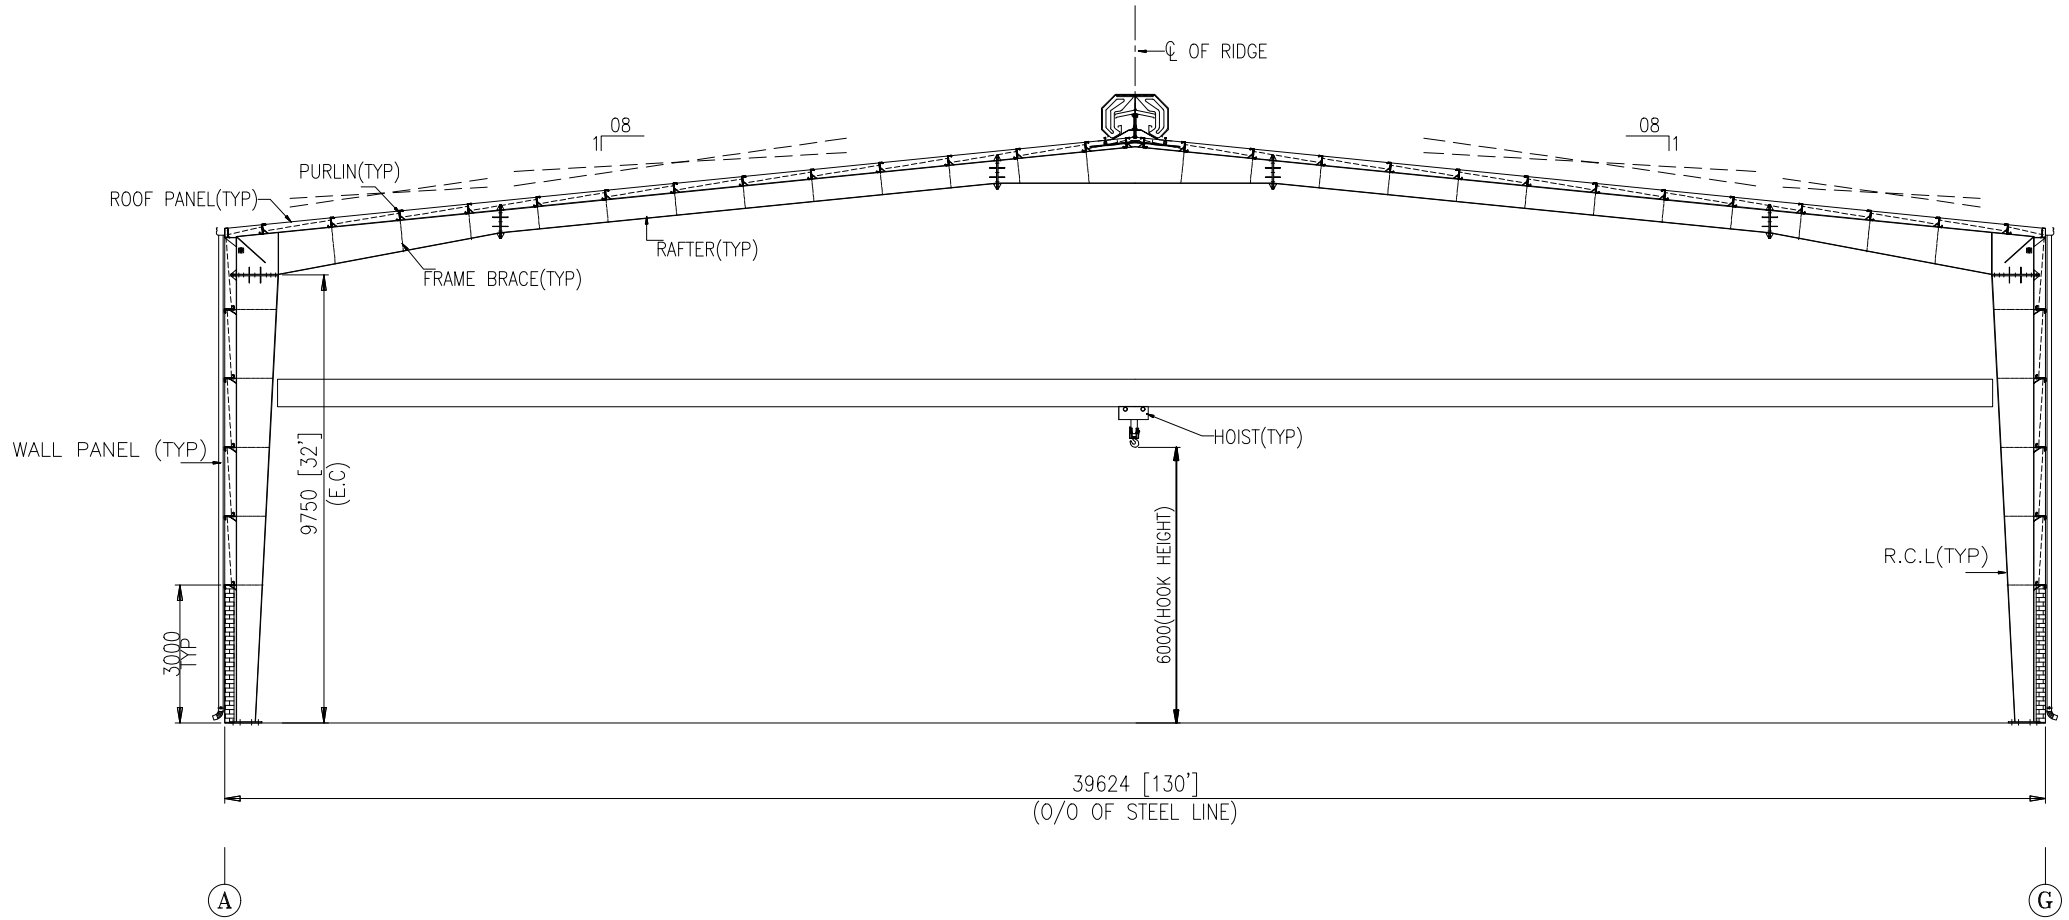


CROSS SECTION AT FRAME LINE-03

NOTE :-

1. ALL DIMENSIONS ARE IN MM U.N.O
2. BASE PLATE SIZE NOT IN TRUE SCALE

TITLE PEB	PROJECT: Fasteners & Allied Products Pvt Ltd, Hubli,				
	CROSS SECTION	DATE 14/01/26	DRAWN AV	APPROVED SA	DRG NO. PR-03
					REV NO. 02

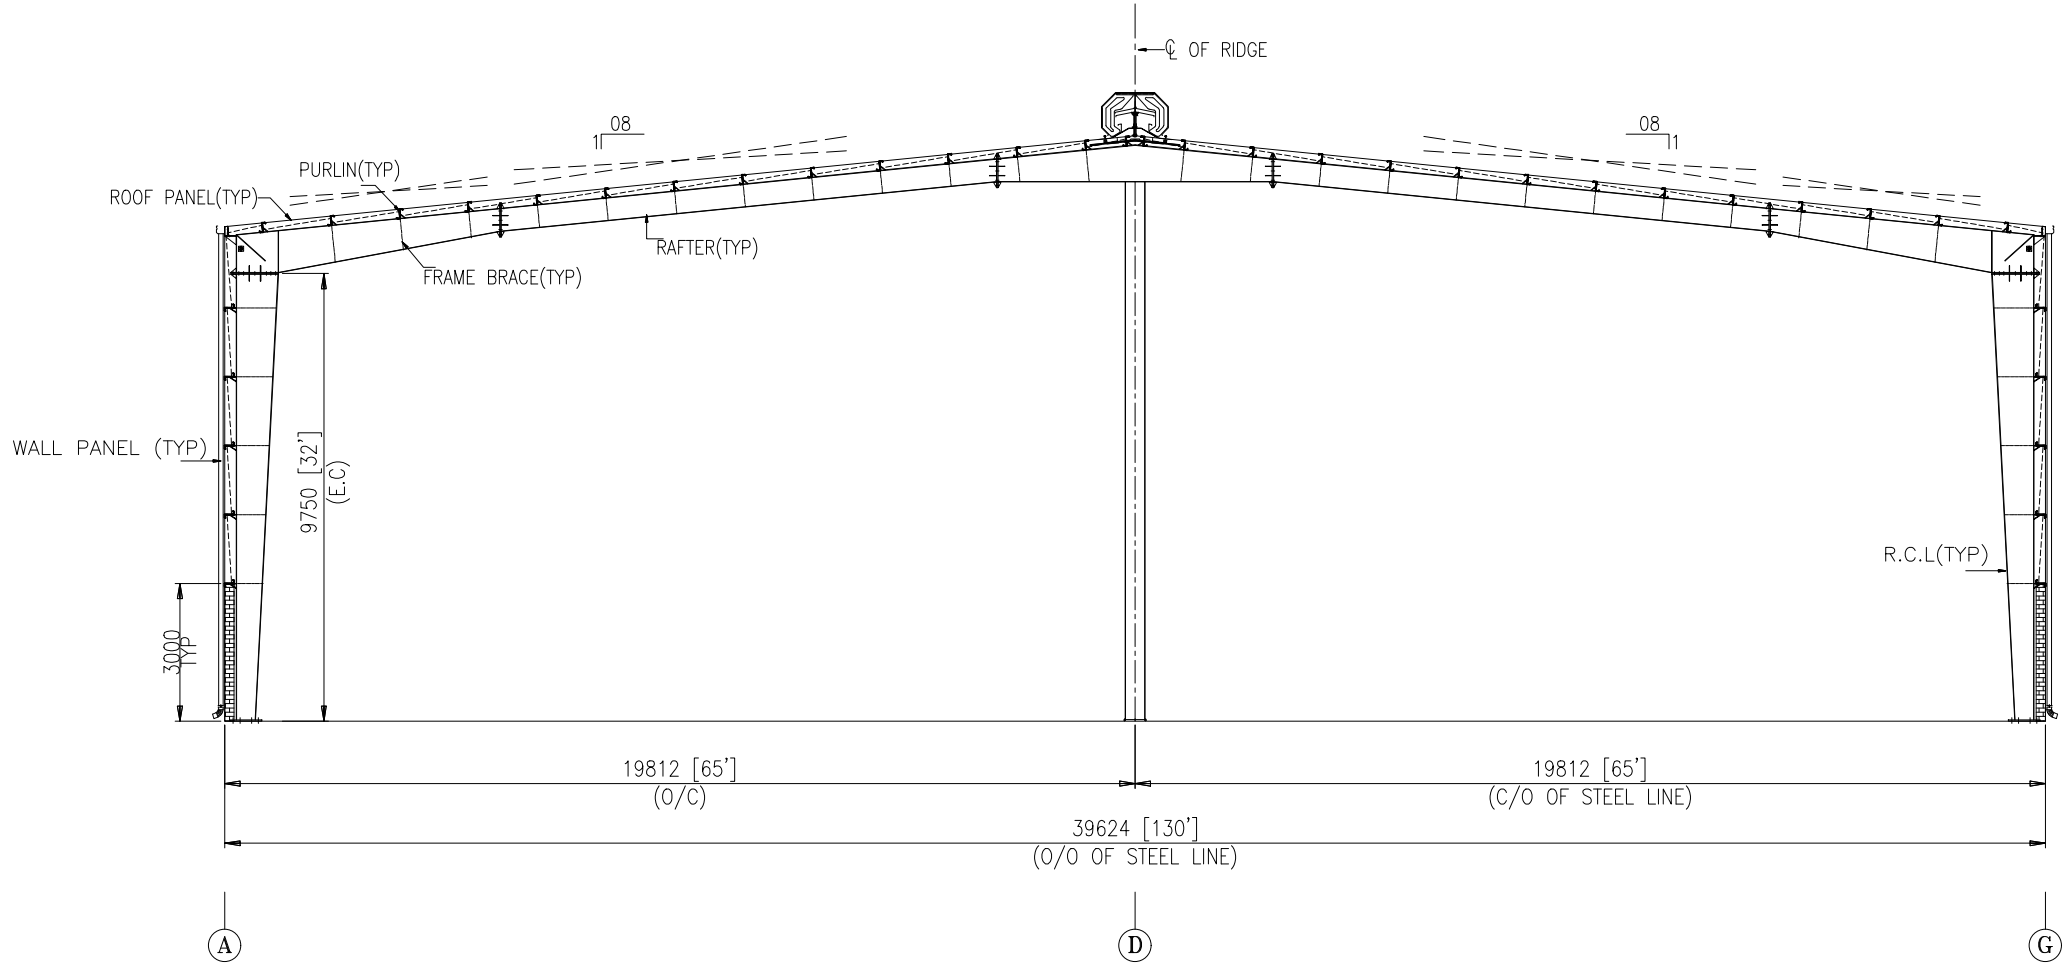


CROSS SECTION AT FRAME LINE-10

NOTE :-

1. ALL DIMENSIONS ARE IN MM U.N.O
2. BASE PLATE SIZE NOT IN TRUE SCALE

TITLE PEB	PROJECT: Fasteners & Allied Products Pvt Ltd, Hubli,				
	CROSS SECTION	DATE 14/01/26	DRAWN AV	APPROVED SA	DRG NO. PR-03
					REV NO. 02

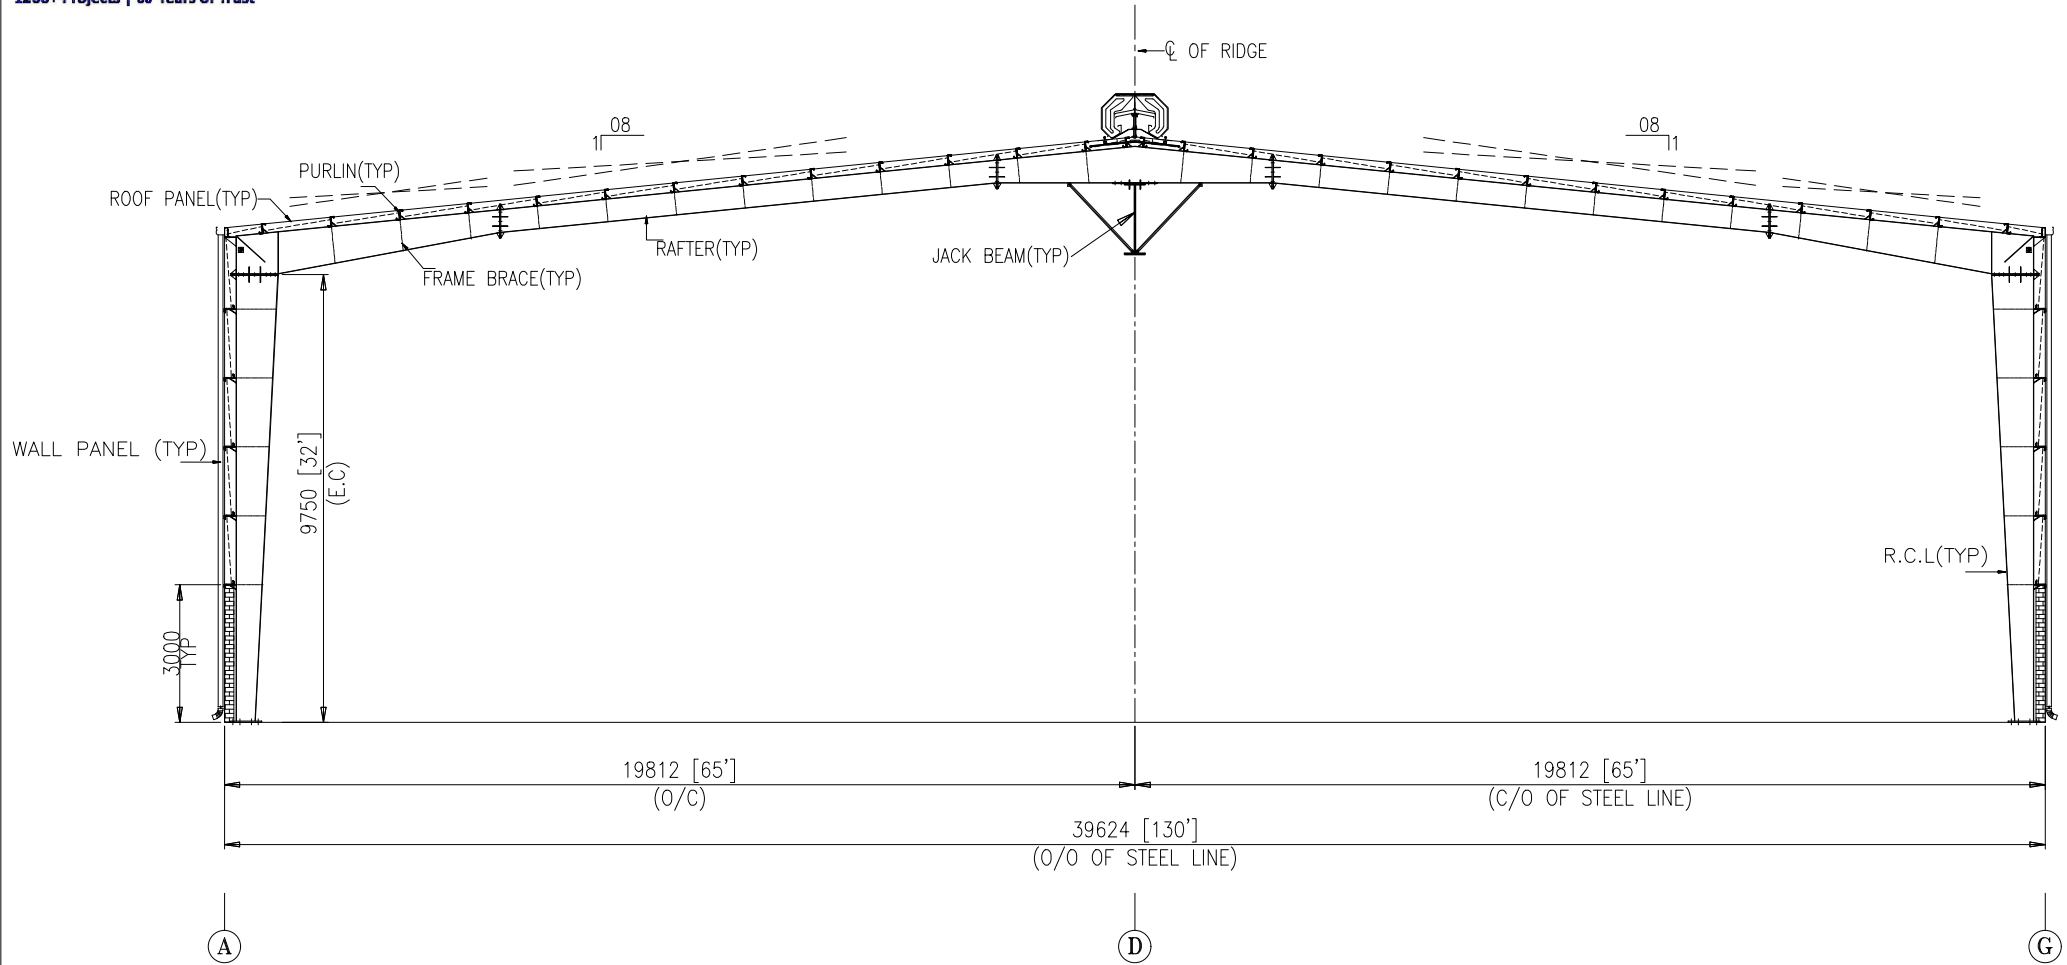

CROSS SECTION AT FRAME LINE-11

NOTE :-

1. ALL DIMENSIONS ARE IN MM U.N.O
2. BASE PLATE SIZE NOT IN TRUE SCALE

TITLE PEB	PROJECT: Fasteners & Allied Products Pvt Ltd, Hubli,				
	CROSS SECTION	DATE 14/01/26	DRAWN AV	APPROVED SA	DRG NO. PR-03
					REV NO. 02